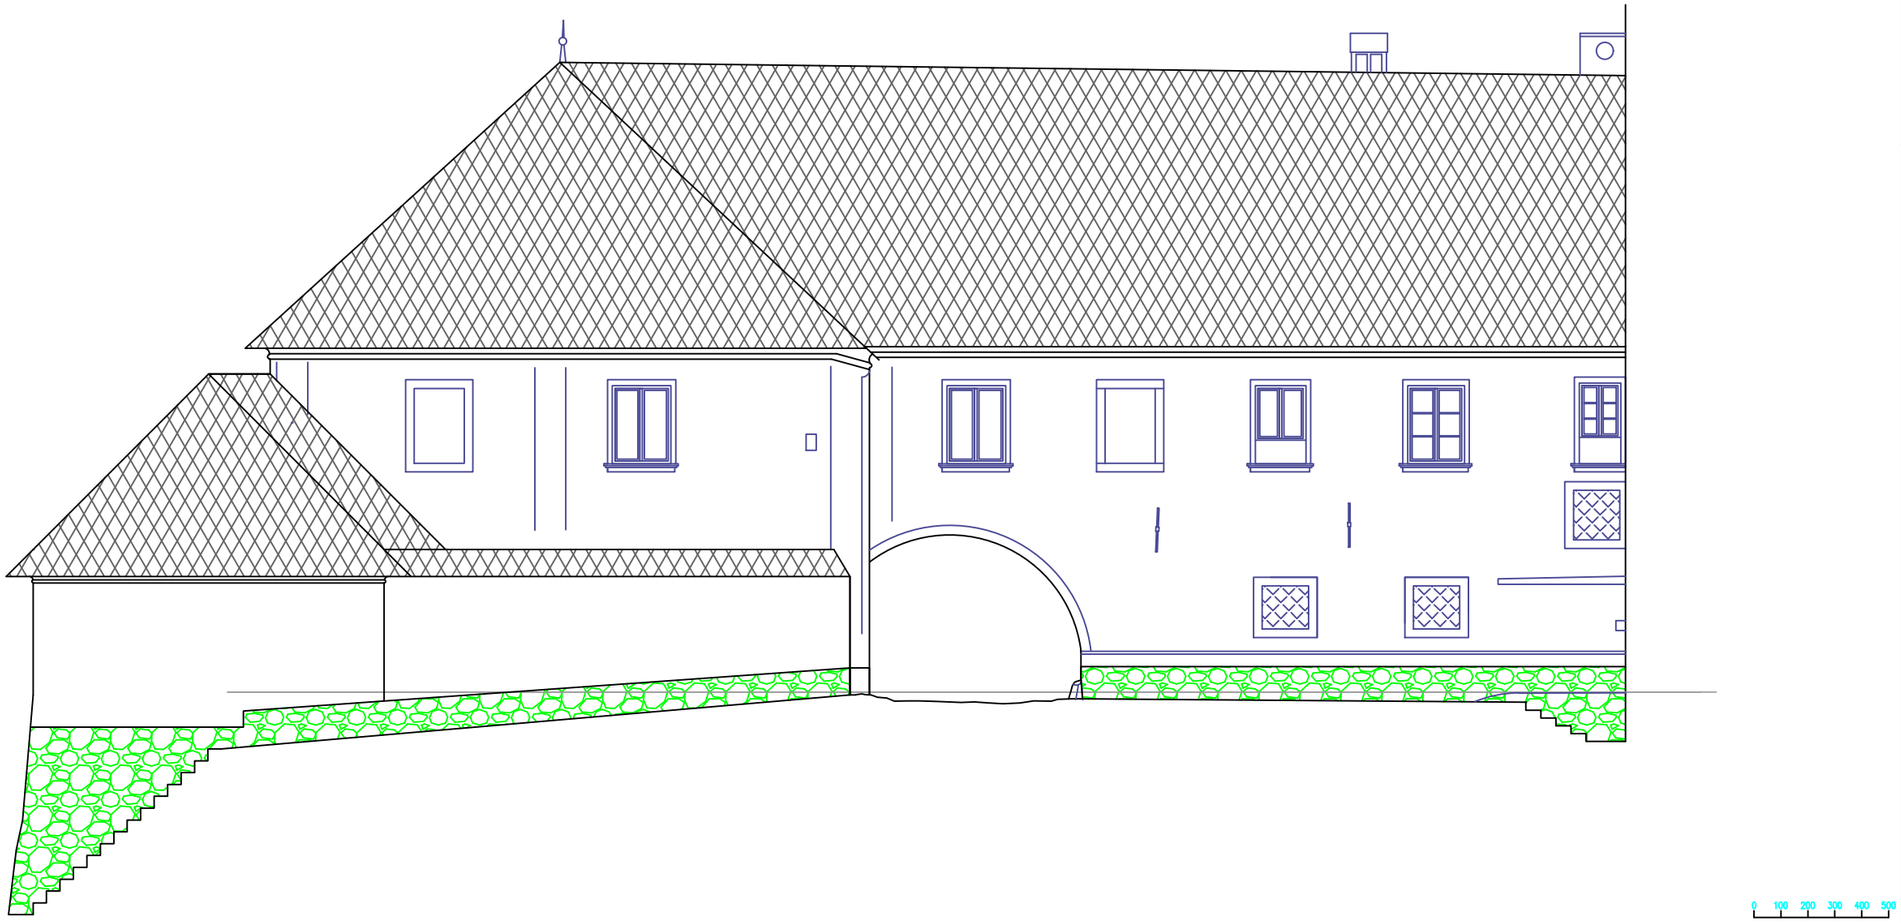

LEGENDA ŠRAFUR:

- OBSTOJEČE STANJE (kamen/opeka)
- ARMIRANI BETON
- BETONSKI MODULAREC
- OPEČNI MODULAREC
- PREDELNE STENE
- AB-ESTRIH
- OBDELAN KAMEN
- LES (beton)
- PREDELNE STENE (mavčno-kartonske plošče)
- IZOLACIJA-mehka
- IZOLACIJA-trda
- ZEMLJINA

GEA CONSULT

GEA CONSULT inženiring, projekt
Mestni trg 5, Škofja Loka
tel/fax (04) 515 74 20 / 515 74 21
GSM 041 667 678, 041 768 555
iden. številka IZS 1208

OBJEKT	STONIČEV GRAD
INVESTITOR	OBČINA ČRNOMELJ, Trg svobode 3
NAČRT	NAČRT ARHITEKTURE
VSEBINA LISTA	ARHITEKTURNA SITUACIJA - VERZ
VODJA PROJEKTA	Aleš Hafner, univ.dipl.inž.arh
POOBLAŠČENI ARHITEKT	Aleš HAFNER, univ.dipl.inž.arh
SODELAVEC	Cene Hafner

št. projekta	datum	faza	merilo	št. lista
B21-036	marec 2023	IDZ	1:50	S5